



# CONTEXTE CUB - PLAN DE CABLAGE GP3

Plan de câblage réalisé par GADONNAUD Ewen et BOINA BOINA Rayan


## PANNEAU DE BRASSAGE

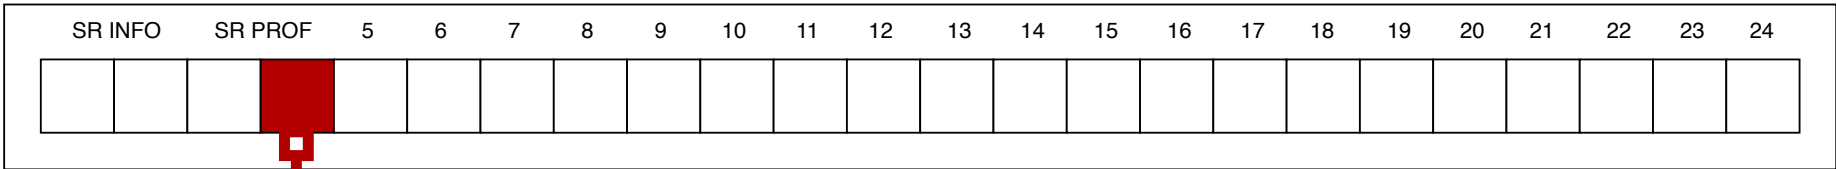


## SWITCH HUAWEI PEDAGOGIQUE

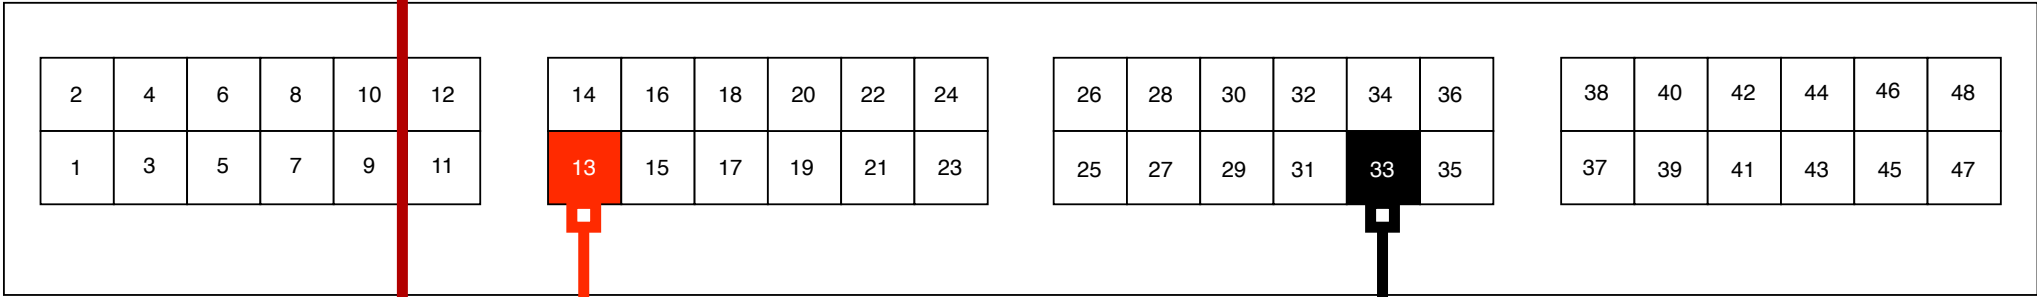


## STORMSHIELD

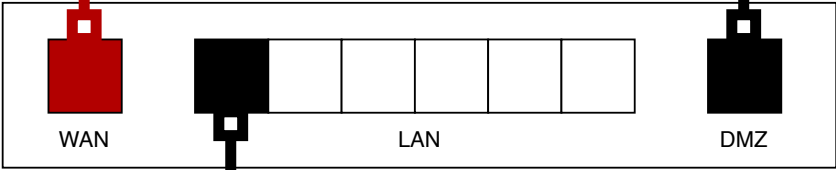

## SWITCH HUAWEI L3 LAN2

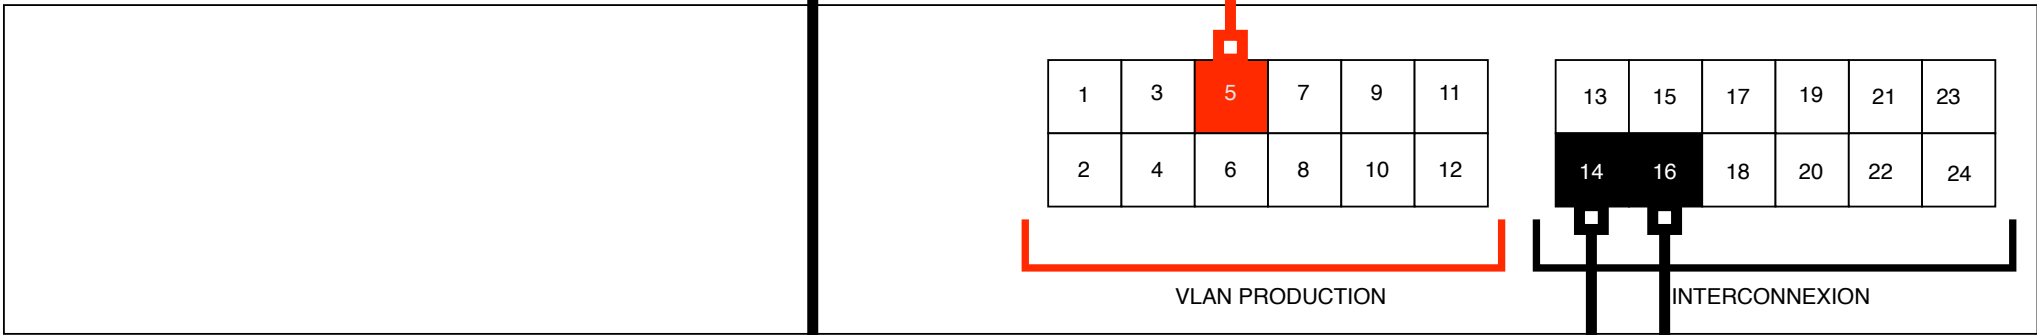

## SWITCH CISCO L2 LAN1

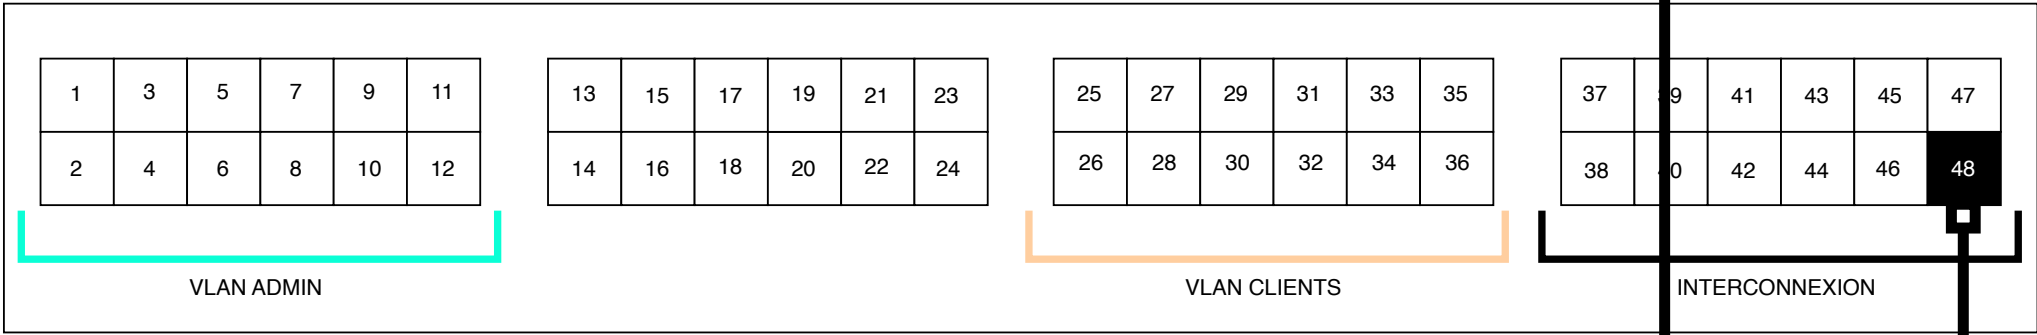

### LÉGENDE

- Liaison WAN / Internet
- Connexion PRODUCTION <-> Projet C
- Ports VLAN PRODUCTION
- Ports VLAN ADMIN
- Ports VLAN CLIENTS
- Ports INTERCONNEXION

### ADRESSAGE

VLAN PRODUCTION : de 51 à 55 (53) -> 172.16.53.1-254  
Passerelle -> 172.16.53.254

DMZ : de 81 à 85 (83)